

POLITECNICO DI MILANO SCUOLA DEL DESIGN C.L. DESIGN DEGLI INTERNI PROGETTO:

QM-D\_2\_CUCINA

CORSO:

STRUMENTI E METODI
DEL PROGETTO

DOCENTE:

MARCO FERRARA

STUDENTI:

OGGETTO: VISTE E ABACO
MOBILE CON
CASSETTI
KNOXHULT
703.268.06

CASSETTI KNOXHULT 703.268.06 DTE:


NOME FILE:
KNOXHULT\_703.268.06.dwg

ERS D.

YYYY.MM.DD

A 744

DATA: **2017/05/23** SCALA: **1:10** REV: **A** FORMATO: **A1** 

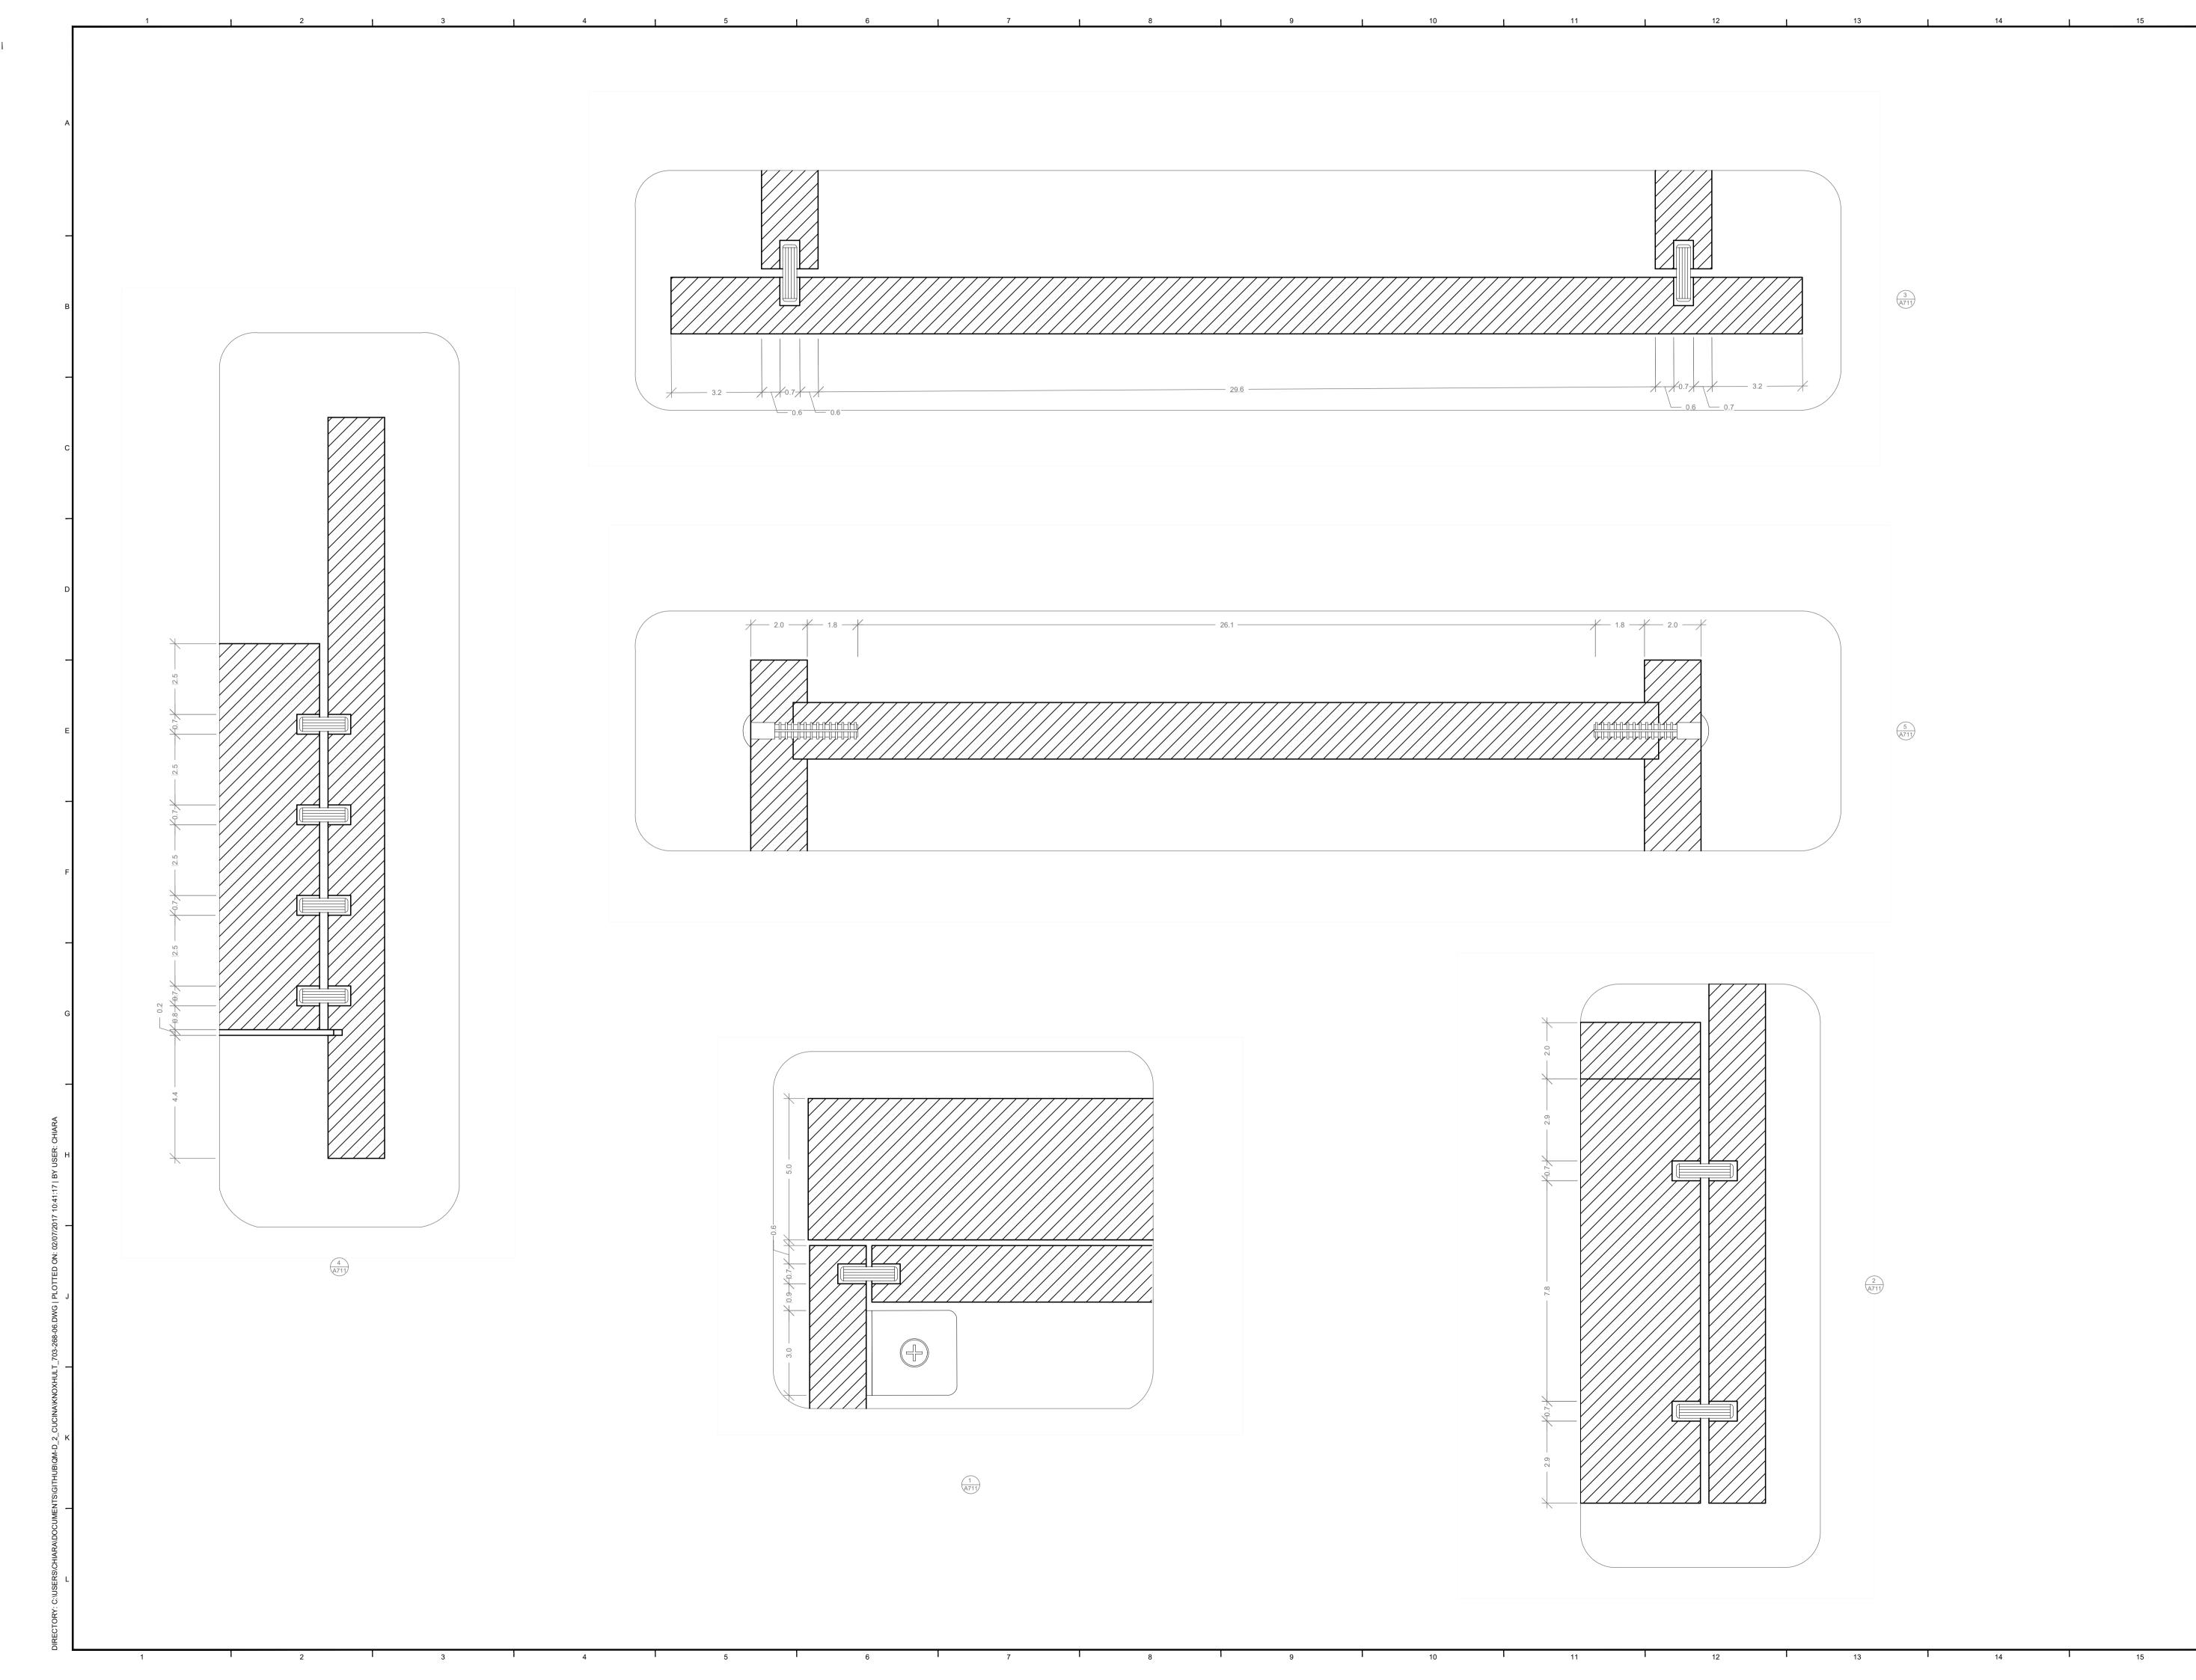

POLITECNICO DI MILANO SCUOLA DEL DESIGN C.L. DESIGN DEGLI INTERNI PROGETTO:

QM-D\_2\_CUCINA

CORSO:

STRUMENTI E METODI
DEL PROGETTO

DOCENTE:

MARCO FERRARA

CHIARA COMBI

STUDENTI:

OGGETTO: DETTAGLI
MOBILE CON
CASSETTI
KNOXHULT
703.268.06

NOME FILE:
KNOXHULT\_703-268-06.dwg

ERS DA

A YYYY.MM.DD

. – . .

A712

DATA: **2017/05/23** SCALA: **1:1** REV: **A** FORMATO: **A1**